PROJECT ROYAL VICTORIA HOSPITAL - HOSPITAL DESIGN
201 GEORGIAN DR, BARRIE, ON L4M 6M2
INDE 3005 - DESIGN COMMUNICATIONS 5

DESIGNED BY: TAYLOR GILES, KAYLA PANTONE, AND CARSEN LEPINE
DESIGNED FOR: FARIBA MOLKI

LIST OF DRAWINGS

SHEET NUMBER	SHEET NAME	SCALE
ID-1	LVL 2 DEMOLITION PLAN	1:100
ID-2	LVL 2 PARTITION PLAN	1:100
ID-3	LVL 2 FURNITURE PLAN	1:100
ID-4	FINISHES PLAN	1:100
ID-5	REFLECTED CEILING PLAN	1:100
ID-6	INTERIOR ELEVATIONS	1:100
ID-7	SECTIONS	1:100
ID-1.1	LVL 3 DEMOLITION PLAN	1:100
ID-1.2	LVL 4 DEMOLITION PLAN	1:100
ID-2.1	LVL 3 PARTITION PLAN	1:100
ID-2.2	LVL 4 PARTITION PLAN	1:100
ID-3.1	LVL 3 FURNITURE PLAN	1:100
ID-3.2	LVL 4 FURNITURE PLAN	1:100
ID-4.2	FINISHES PLAN	1:100
ID-00	COVER PAGE	1:100
ID-5.1	REFLECTED CEILING PLAN	1:100
ID-4.1	FINISHES PLAN	1:100



Design ATELIER

(705) 826-4206
1 GEORGIAN DR. BARRIE, ON

GENERAL NOTES:

1. THE CONTRACTOR AND ALL SUB-CONTRACTORS SHALL VERIFY ALL DIMENSIONS, DETAILS AND SPECIFICATIONS ON SITE AND REPORT ALL DISCREPANCIES IN WRITING TO THE DESIGNER BEFORE PROCEEDING WITH THE WORK.
2. DRAWINGS ARE NOT TO BE SCALED.
3. THE CONTRACTOR AND SUB-CONTRACTORS, BEFORE PROCEEDING WITH THE WORK, MUST SUBMIT ALL NECESSARY SAMPLES AND SHOP DRAWINGS TO THE DESIGNER FOR APPROVAL.
4. ALL CONCEPTS, DESIGNS, DETAILS, DRAWINGS AND SPECIFICATIONS ARE STUDENT WORK AND THE PROPERTY OF THE DESIGNER. AS SUCH, THEY ARE NOT INTENDED FOR USE ON OTHER PROJECTS OR EXTENSIONS OF THE SPECIFIED PROJECT WHATSOEVER.

OWNERSHIP: ALL DRAWINGS, SPECIFICATIONS, DESIGNS & COPIES THEROF ARE THE PROPERTY OF THE DESIGNER AND THE OWNER, WHETHER OR NOT THE WORK FOR WHICH THEY ARE MADE IS PERFORMED, AND ARE NOT TO BE USED OR DUPLICATED ON OTHER WORK EXCEPT BY WRITTEN CONSENT FROM THE DESIGNER AND OWNER.

REV	DESCRIPTION	DATE

PROJECT:
ROYAL VICTORIA REGIONAL HEALTH CENTRE

ADDRESS:
201 GEORGIAN DR.
BARRIE, ON L4M 6M2

DRAWING:
COVER PAGE

SHEET:
ID-00

DESIGNED BY:
KP, CL, TG

ISSUE DATE:
04.09.2026


COURSE:
INDE 3005

SCALE:

2026-11-06 2:26:15 PM

ALL EXISTING WINDOWS, WALLS, AND DOORS ARE NOT TO BE DEMOLISHED AND TO REMAIN.

STAIRS ARE TO BE DEMOLISHED.

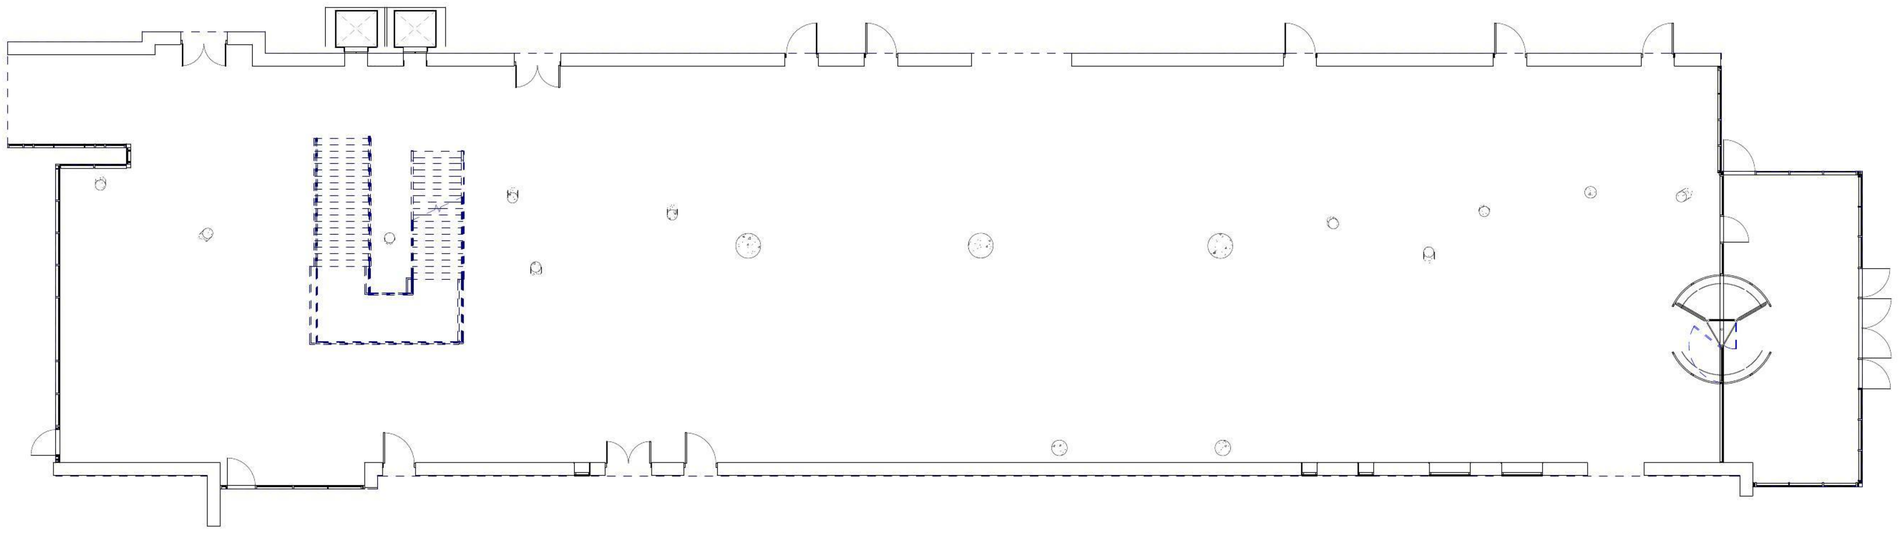

1 LVL 2 DEMOLITION PLAN

1 : 100

- - - - - - - DEMOLISHED

Design ATELIER

(705) 826-4206
1 GEORGIAN DR. BARRIE, ON

GENERAL NOTES:

1. THE CONTRACTOR AND ALL SUB-CONTRACTORS SHALL VERIFY ALL DIMENSIONS, DETAILS AND SPECIFICATIONS ON SITE AND REPORT ALL DISCREPANCIES IN WRITING TO THE DESIGNER BEFORE PROCEEDING WITH THE WORK.
2. DRAWINGS ARE NOT TO BE SCALED.
3. THE CONTRACTOR AND SUB-CONTRACTORS, BEFORE PROCEEDING WITH THE WORK, MUST SUBMIT ALL NECESSARY SAMPLES AND SHOP DRAWINGS TO THE DESIGNER FOR APPROVAL.
4. ALL CONCEPTS, DESIGNS, DETAILS, DRAWINGS AND SPECIFICATIONS ARE STUDENT WORK AND THE PROPERTY OF THE DESIGNER. AS SUCH, THEY ARE NOT INTENDED FOR USE ON OTHER PROJECTS OR EXTENSIONS OF THE SPECIFIED PROJECT WHATSOEVER.

OWNERSHIP: ALL DRAWINGS, SPECIFICATIONS, DESIGNS & COPIES THEROF ARE THE PROPERTY OF THE DESIGNER AND THE OWNER, WHETHER OR NOT THE WORK FOR WHICH THEY ARE MADE IS PERFORMED, AND ARE NOT TO BE USED OR DUPLICATED ON OTHER WORK EXCEPT BY WRITTEN CONSENT FROM THE DESIGNER AND OWNER.

REV	DESCRIPTION	DATE

PROJECT:
ROYAL VICTORIA REGIONAL HEALTH CENTRE

ADDRESS:
201 GEORGIAN DR.
BARRIE, ON L4M 6M2

DRAWING:
LVL 2 DEMOLITION PLAN

SHEET:
ID-1

DESIGNED BY:
KP, CL, TG

ISSUE DATE:
04.09.2026

COURSE:
INDE 3005


SCALE:
1 : 100

2026-11-08 2:26:16 PM

ALL EXISTING WALLS AND DOORS ARE NOT TO BE DEMOLISHED AND TO REMAIN.

STAIRS ARE TO BE DEMOLISHED.

3RD AND 4TH FLOORS WILL BE EXTENDED OVER.

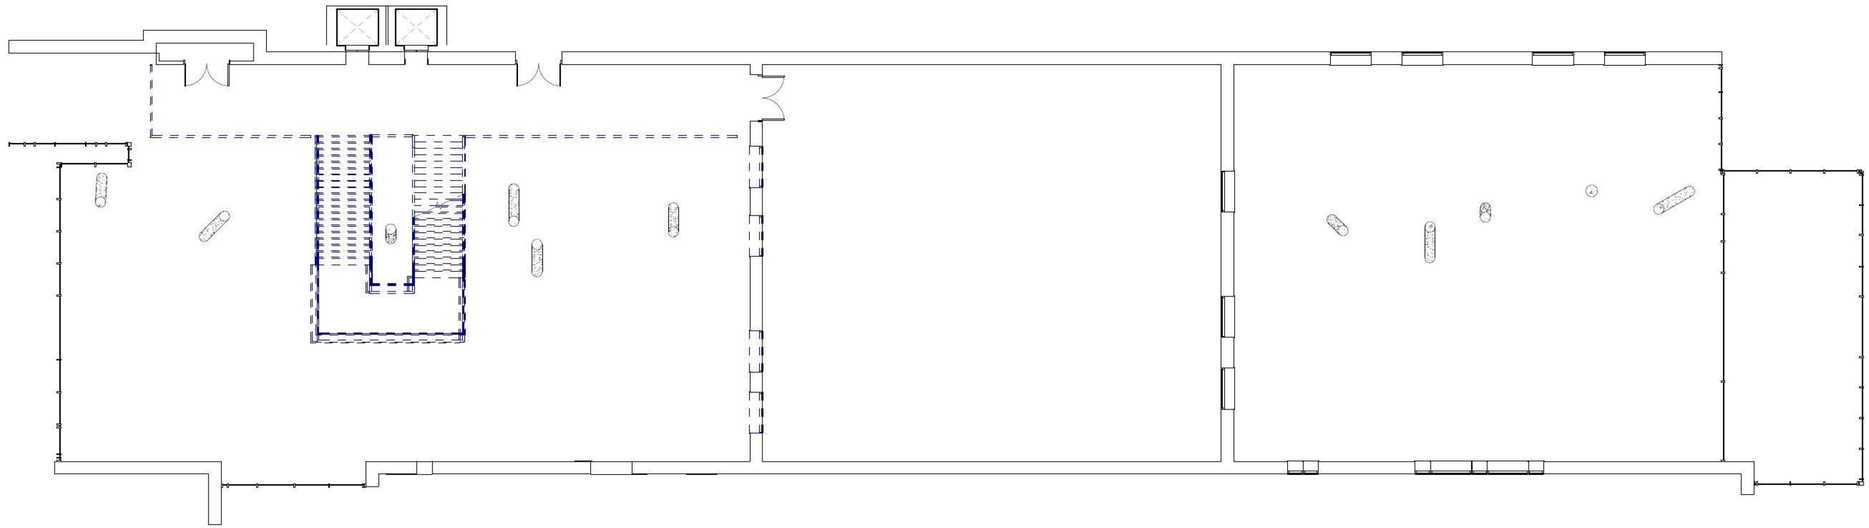

1 LVL 3 DEMOLITION PLAN

1 : 100

- - - - - - - DEMOLISHED

Design ATELIER

(705) 826-4206
1 GEORGIAN DR. BARRIE, ON

GENERAL NOTES:

1. THE CONTRACTOR AND ALL SUB-CONTRACTORS SHALL VERIFY ALL DIMENSIONS, DETAILS AND SPECIFICATIONS ON SITE AND REPORT ALL DISCREPANCIES IN WRITING TO THE DESIGNER BEFORE PROCEEDING WITH THE WORK.
2. DRAWINGS ARE NOT TO BE SCALED.
3. THE CONTRACTOR AND SUB-CONTRACTORS, BEFORE PROCEEDING WITH THE WORK, MUST SUBMIT ALL NECESSARY SAMPLES AND SHOP DRAWINGS TO THE DESIGNER FOR APPROVAL.
4. ALL CONCEPTS, DESIGNS, DETAILS, DRAWINGS AND SPECIFICATIONS ARE STUDENT WORK AND THE PROPERTY OF THE DESIGNER. AS SUCH, THEY ARE NOT INTENDED FOR USE ON OTHER PROJECTS OR EXTENSIONS OF THE SPECIFIED PROJECT WHATSOEVER.

OWNERSHIP. ALL DRAWINGS, SPECIFICATIONS, DESIGNS & COPIES THEROF ARE THE PROPERTY OF THE DESIGNER AND THE OWNER, WHETHER OR NOT THE WORK FOR WHICH THEY ARE MADE IS PERFORMED, AND ARE NOT TO BE USED OR DUPLICATED ON OTHER WORK EXCEPT BY WRITTEN CONSENT FROM THE DESIGNER AND OWNER.

REV	DESCRIPTION	DATE

PROJECT: ROYAL VICTORIA REGIONAL HEALTH CENTRE

ADDRESS: 201 GEORGIAN DR. BARRIE, ON L4M 6M2

DRAWING: LVL 3 DEMOLITION PLAN

SHEET: ID-1.1

DESIGNED BY: KP, CL, TG

ISSUE DATE: 04.09.2026

COURSE: INDE 3005


SCALE: 1 : 100

2026-11-08 2:26:17 PM

ALL EXISTING WALLS AND DOORS ARE NOT TO BE DEMOLISHED AND TO REMAIN.

STAIRS ARE TO BE DEMOLISHED.

3RD AND 4TH FLOORS WILL BE EXTENDED OVER

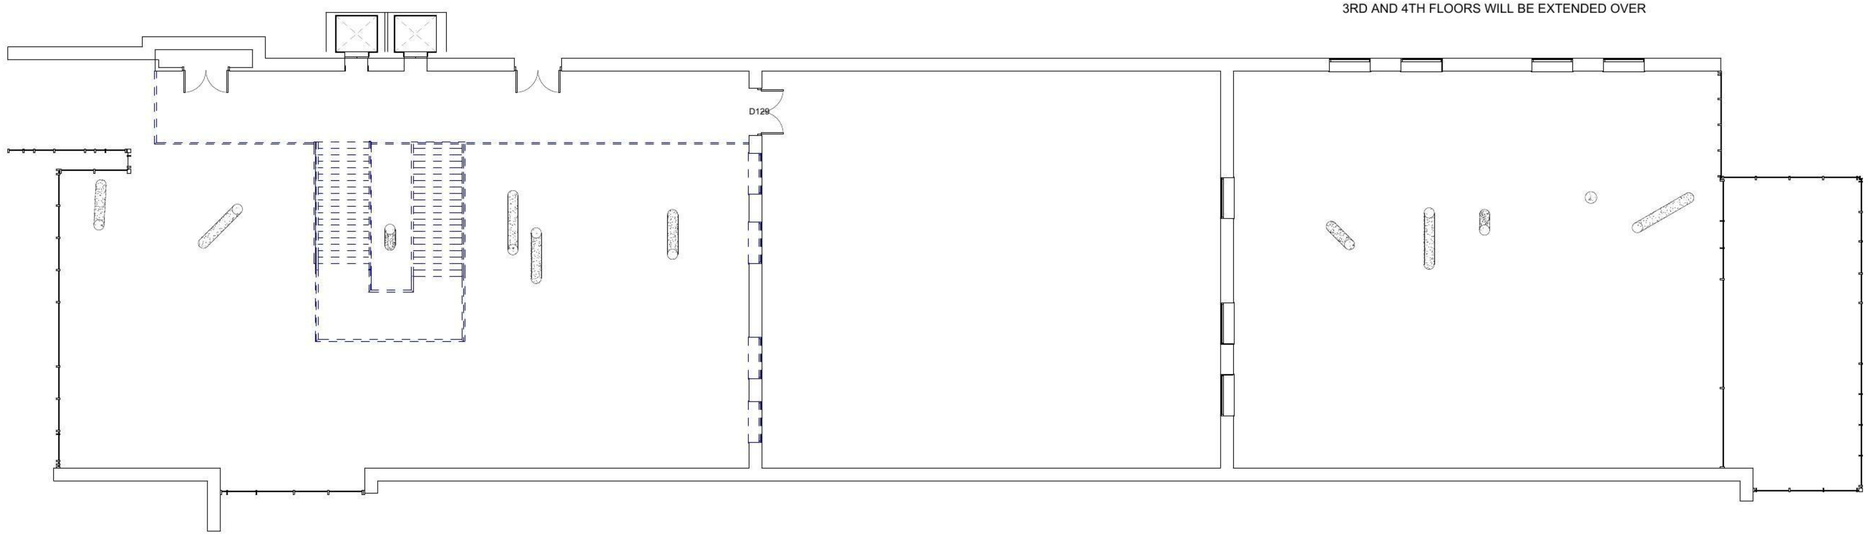

1 LVL 4 DEMOLITION PLAN

1 : 100

– – – – – – – DEMOLISHED

Design ATELIER

(705) 826-4266
1 GEORGIAN DR. BARRIE, ON

GENERAL NOTES:

1. THE CONTRACTOR AND ALL SUB-CONTRACTORS SHALL VERIFY ALL DIMENSIONS, DETAILS AND SPECIFICATIONS ON SITE AND REPORT ALL DISCREPANCIES IN WRITING TO THE DESIGNER BEFORE PROCEEDING WITH THE WORK.
2. DRAWINGS ARE NOT TO BE SCALED.
3. THE CONTRACTOR AND SUB-CONTRACTORS, BEFORE PROCEEDING WITH THE WORK, MUST SUBMIT ALL NECESSARY SAMPLES AND SHOP DRAWINGS TO THE DESIGNER FOR APPROVAL.
4. ALL CONCEPTS, DESIGNS, DETAILS, DRAWINGS AND SPECIFICATIONS ARE STUDENT WORK, AND THE PROPERTY OF THE DESIGNER. AS SUCH, THEY ARE NOT INTENDED FOR USE ON OTHER PROJECTS OR EXTENSIONS OF THE SPECIFIED PROJECT WHATSOEVER.

OWNERSHIP. ALL DRAWINGS, SPECIFICATIONS, DESIGNS & COPIES THEROF ARE THE PROPERTY OF THE DESIGNER AND THE OWNER, WHETHER OR NOT THE WORK FOR WHICH THEY ARE MADE IS PERFORMED, AND ARE NOT TO BE USED OR DUPLICATED ON OTHER WORK EXCEPT BY WRITTEN CONSENT FROM THE DESIGNER AND OWNER.

REV	DESCRIPTION	DATE

PROJECT: ROYAL VICTORIA REGIONAL HEALTH CENTRE

ADDRESS: 201 GEORGIAN DR.
BARRIE, ON L4M 6M2

DRAWING: LVL 4 DEMOLITION PLAN

SHEET: ID-1.2


DESIGNED BY: KP, CL, TG

ISSUE DATE: 04.09.2026

COURSE: INDE 3005

SCALE: 1 : 100

2026-11-08 2:26:17 PM

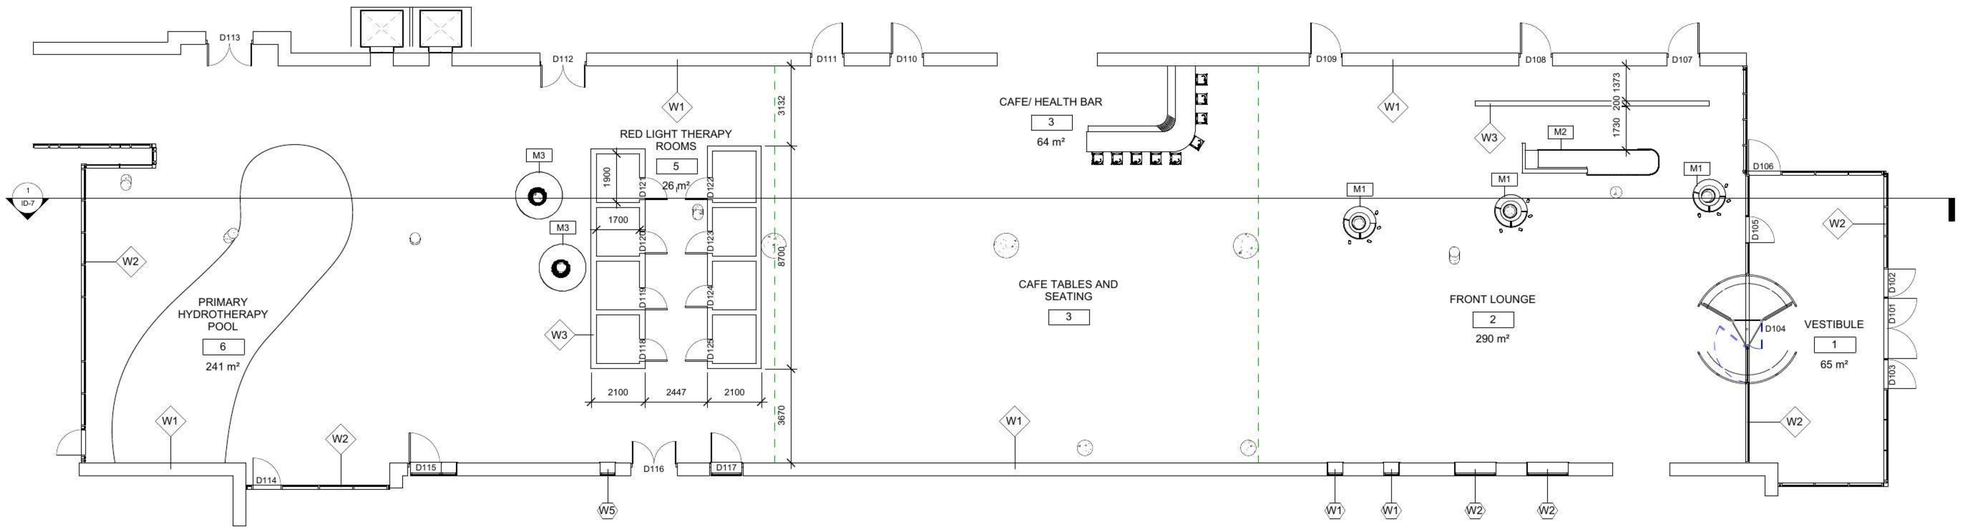

1 LVL 2 PARTITION PLAN

1 : 100

Casework and Milwork Schedule				
Tag	Description	Materials	Manufacturer	Quantity
M1	Reception Desk	Wood base Quartz countertop	Custom	1
M2	Sanitization Station	Concrete	Custom	3
M3	Column Seating	Concrete Linen Upholstery	Custom	2

Design ATELIER
(705) 826-4206
1 GEORGIAN DR. BARRIE, ON

GENERAL NOTES:

1. THE CONTRACTOR AND ALL SUB-CONTRACTORS SHALL VERIFY ALL DIMENSIONS, DETAILS AND SPECIFICATIONS ON SITE AND REPORT ALL DISCREPANCIES IN WRITING TO THE DESIGNER BEFORE PROCEEDING WITH THE WORK.
2. DRAWINGS ARE NOT TO BE SCALED.
3. THE CONTRACTOR AND SUB-CONTRACTORS, BEFORE PROCEEDING WITH THE WORK, MUST SUBMIT ALL NECESSARY SAMPLES AND SHOP DRAWINGS TO THE DESIGNER FOR APPROVAL.
4. ALL CONCEPTS, DESIGNS, DETAILS, DRAWINGS AND SPECIFICATIONS ARE STUDENT WORK AND THE PROPERTY OF THE DESIGNER. AS SUCH, THEY ARE NOT INTENDED FOR USE ON OTHER PROJECTS OR EXTENSIONS OF THE SPECIFIED PROJECT WHATSOEVER.

OWNERSHIP: ALL DRAWINGS, SPECIFICATIONS, DESIGNS & COPIES THEROF ARE THE PROPERTY OF THE DESIGNER AND THE OWNER, WHETHER OR NOT THE WORK FOR WHICH THEY ARE MADE IS PERFORMED, AND ARE NOT TO BE USED OR DUPLICATED ON OTHER WORK EXCEPT BY WRITTEN CONSENT FROM THE DESIGNER AND OWNER.

REV	DESCRIPTION	DATE

PROJECT:
ROYAL VICTORIA REGIONAL HEALTH CENTRE

ADDRESS:
201 GEORGIAN DR.
BARRIE, ON L4M 6M2

DRAWING:
LVL 2 PARTITION PLAN

SHEET:
ID-2


DESIGNED BY:
KP, CL, TG

ISSUE DATE:
04.09.2026

COURSE:
INDE 3005

SCALE:
As indicated

2026-11-08 2:26:24 PM

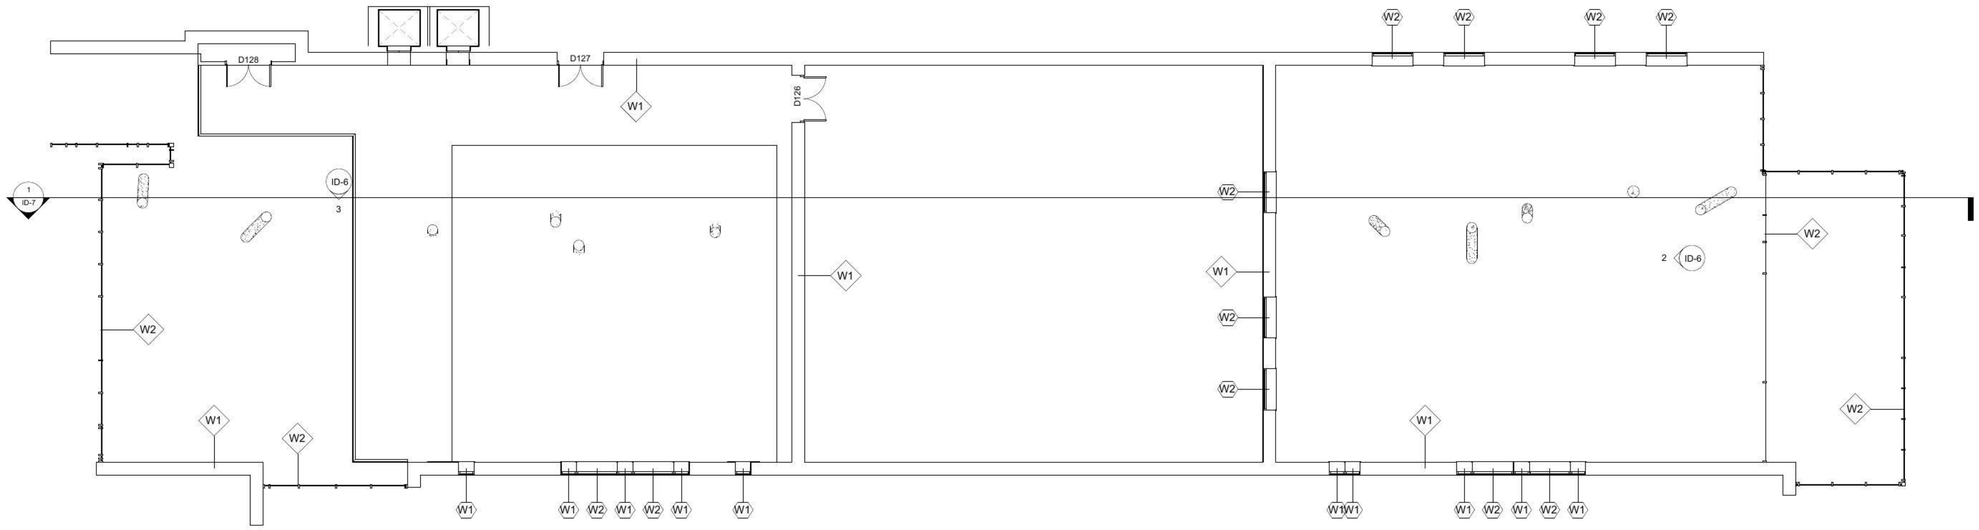

1 LVL 3 PARTITION PLAN
1 : 100

Casework and Milwork Schedule				
Tag	Description	Materials	Manufacturer	Quantity
M1	Reception Desk	Wood base Quartz countertop	Custom	1
M2	Sanitization Station	Concrete	Custom	3
M3	Column Seating	Concrete Linen Upholstery	Custom	2

Design ATELIER
(705) 826-4206
1 GEORGIAN DR. BARRIE, ON

GENERAL NOTES:

1. THE CONTRACTOR AND ALL SUB-CONTRACTORS SHALL VERIFY ALL DIMENSIONS, DETAILS AND SPECIFICATIONS ON SITE AND REPORT ALL DISCREPANCIES IN WRITING TO THE DESIGNER BEFORE PROCEEDING WITH THE WORK.
2. DRAWINGS ARE NOT TO BE SCALED.
3. THE CONTRACTOR AND SUB-CONTRACTORS, BEFORE PROCEEDING WITH THE WORK, MUST SUBMIT ALL NECESSARY SAMPLES AND SHOP DRAWINGS TO THE DESIGNER FOR APPROVAL.
4. ALL CONCEPTS, DESIGNS, DETAILS, DRAWINGS AND SPECIFICATIONS ARE STUDENT WORK AND THE PROPERTY OF THE DESIGNER. AS SUCH, THEY ARE NOT INTENDED FOR USE ON OTHER PROJECTS OR EXTENSIONS OF THE SPECIFIED PROJECT WHATSOEVER.

OWNERSHIP. ALL DRAWINGS, SPECIFICATIONS, DESIGNS & COPIES THEROF ARE THE PROPERTY OF THE DESIGNER AND THE OWNER, WHETHER OR NOT THE WORK FOR WHICH THEY ARE MADE IS PERFORMED, AND ARE NOT TO BE USED OR DUPLICATED ON OTHER WORK EXCEPT BY WRITTEN CONSENT FROM THE DESIGNER AND OWNER.

REV	DESCRIPTION	DATE

PROJECT:
ROYAL VICTORIA REGIONAL HEALTH CENTRE

ADDRESS:
201 GEORGIAN DR.
BARRIE, ON L4M 6M2

DRAWING:
LVL 3 PARTITION PLAN

SHEET:
ID-2.1


DESIGNED BY:
KP, CL, TG

ISSUE DATE:
04.09.2026

COURSE:
INDE 3005

SCALE:
As indicated

2026-11-08 2:26:25 PM

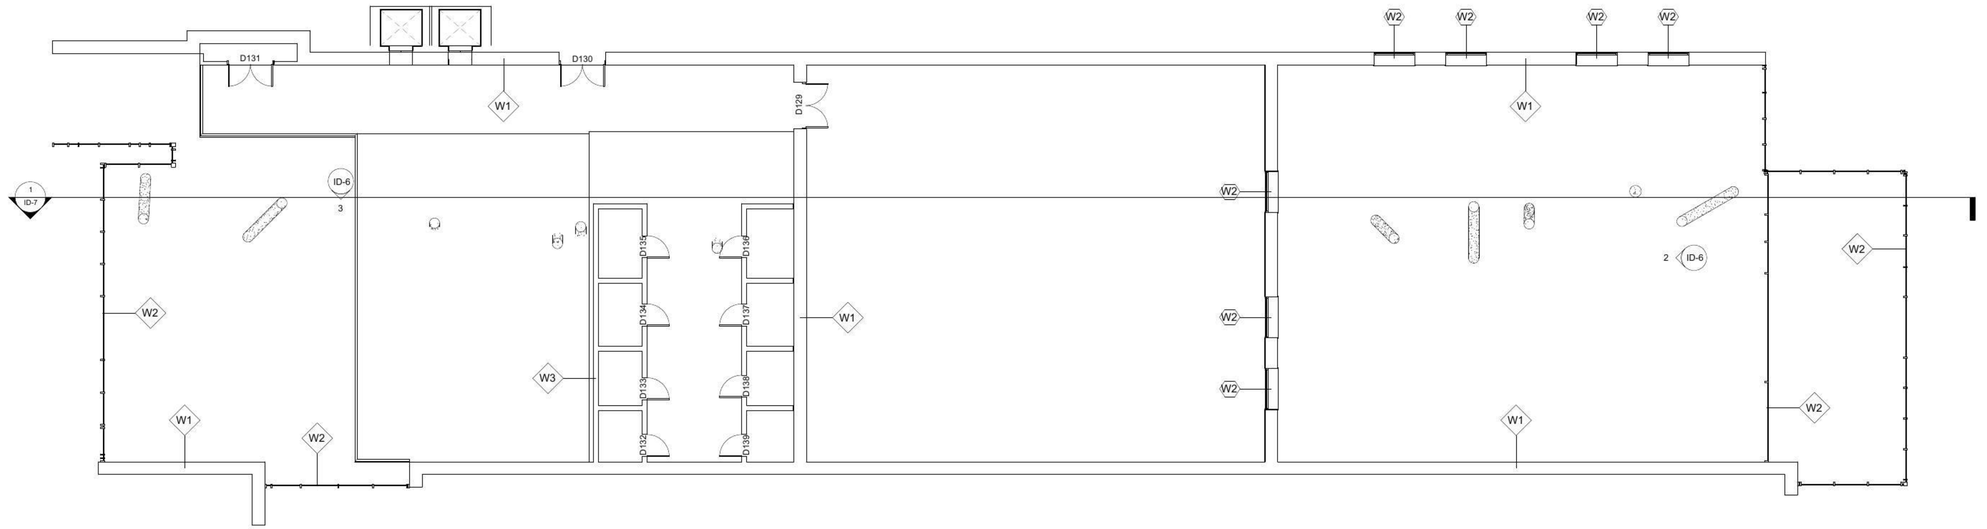

1 LVL 4 PARTITION PLAN
1 : 100

Casework and Milwork Schedule				
Tag	Description	Materials	Manufacturer	Quantity
M1	Reception Desk	Wood base Quartz countertop	Custom	1
M2	Sanitization Station	Concrete	Custom	3
M3	Column Seating	Concrete Linen Upholstery	Custom	2

Design ATELIER
(705) 826-4206
1 GEORGIAN DR. BARRIE, ON

GENERAL NOTES:

1. THE CONTRACTOR AND ALL SUB-CONTRACTORS SHALL VERIFY ALL DIMENSIONS, DETAILS AND SPECIFICATIONS ON SITE AND REPORT ALL DISCREPANCIES IN WRITING TO THE DESIGNER BEFORE PROCEEDING WITH THE WORK.
2. DRAWINGS ARE NOT TO BE SCALED.
3. THE CONTRACTOR AND SUB-CONTRACTORS, BEFORE PROCEEDING WITH THE WORK, MUST SUBMIT ALL NECESSARY SAMPLES AND SHOP DRAWINGS TO THE DESIGNER FOR APPROVAL.
4. ALL CONCEPTS, DESIGNS, DETAILS, DRAWINGS AND SPECIFICATIONS ARE STUDENT WORK AND THE PROPERTY OF THE DESIGNER. AS SUCH, THEY ARE NOT INTENDED FOR USE ON OTHER PROJECTS OR EXTENSIONS OF THE SPECIFIED PROJECT WHATSOEVER.

OWNERSHIP. ALL DRAWINGS, SPECIFICATIONS, DESIGNS & COPIES THEROF ARE THE PROPERTY OF THE DESIGNER AND THE OWNER, WHETHER OR NOT THE WORK FOR WHICH THEY ARE MADE IS PERFORMED, AND ARE NOT TO BE USED OR DUPLICATED ON OTHER WORK EXCEPT BY WRITTEN CONSENT FROM THE DESIGNER AND OWNER.

REV	DESCRIPTION	DATE

PROJECT: ROYAL VICTORIA REGIONAL HEALTH CENTRE

ADDRESS: 201 GEORGIAN DR.
BARRIE, ON L4M 6M2

DRAWING: LVL 4 PARTITION PLAN

SHEET: ID-2.2


DESIGNED BY: KP, CL, TG

ISSUE DATE: 04.09.2026

COURSE: INDE 3005

SCALE: As indicated

2026-11-08 2:26:26 PM

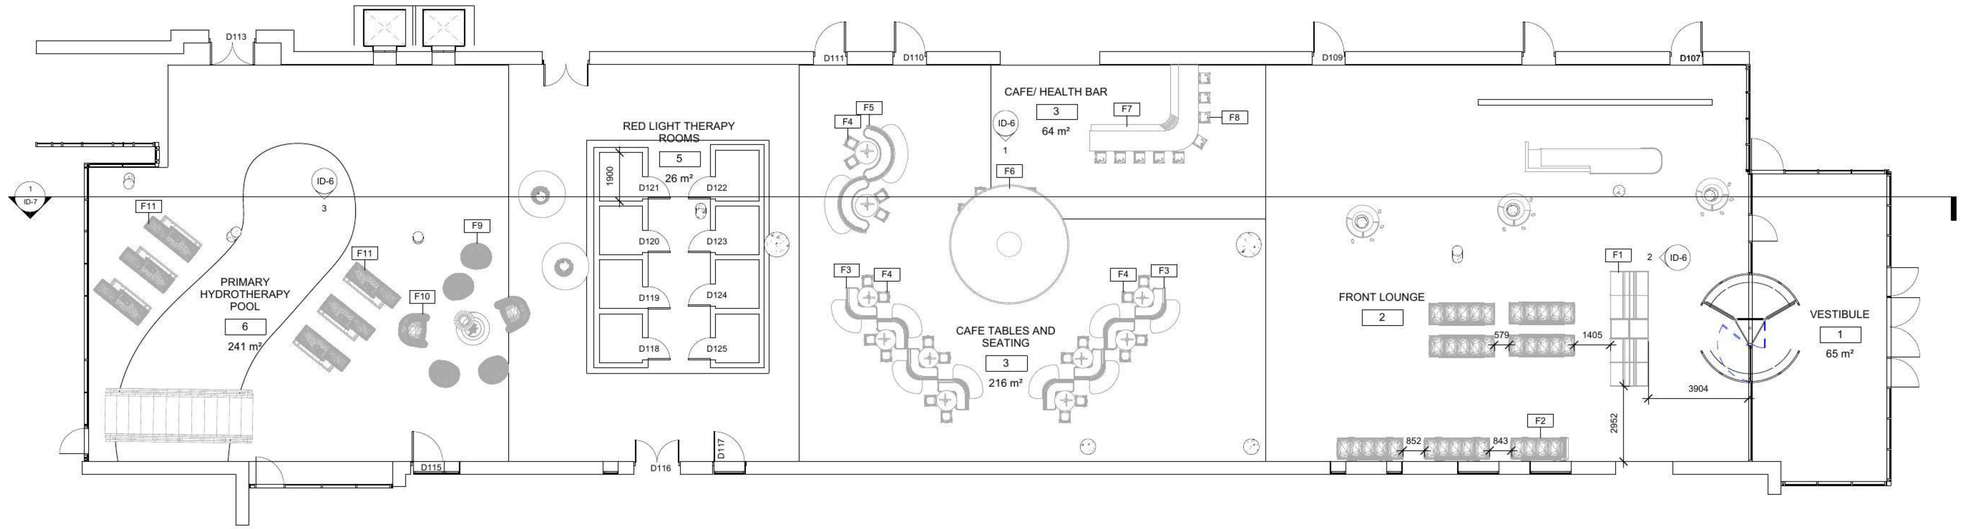

1 LVL 2 FURNITURE PLAN

1 : 100

FF&E Schedule

Tag	Description	Materials	Manufacturer	Quantity
F1	Sofa w Built-In Table	Polyester, Maple Finish	Stance Healthcare	1
F2	Accessible Sofa	Cotton, Maple Wood	Custom	7
F3	Cafe Booths	Plastic(PTFE), Maple Wood	Custom	8
F4	Cafe Seating	Stainless Steel(Black), Wood	Steelcase Health	20
F5	Rounded Cafe Booths	Plastic(PTFE), Maple Wood	Custom	2
F6	Architectural Built-In	Maple Wood	Custom	1
F7	Built-In Bar	Maple Wood, Cladded	Medmill	1
F9	Bar Seating	Stainless Steel(Black), Wood	Steelcase Health	9
F10	Beanbag Seating	Polyester, Cotton	Stance Healthcare	4
F11	Armchair	Cotton, Maple Wood Finish	Stance Healthcare	2
F12	Reclining 'Beach' Chair	Cotton, Maple Wood	Stance Healthcare	6
F13	Sauna	Cedar, Hemlock	True North Saunas	4
F14	Cold Plunge	Stainless Steel, Cedar	IceWorksBath	4

Design ATELIER
(705) 826-4266
1 GEORGIAN DR. BARRIE, ON

GENERAL NOTES:

1. THE CONTRACTOR AND ALL SUB-CONTRACTORS SHALL VERIFY ALL DIMENSIONS, DETAILS AND SPECIFICATIONS ON SITE AND REPORT ALL DISCREPANCIES IN WRITING TO THE DESIGNER BEFORE PROCEEDING WITH THE WORK.
2. DRAWINGS ARE NOT TO BE SCALED.
3. THE CONTRACTOR AND SUB-CONTRACTORS, BEFORE PROCEEDING WITH THE WORK, MUST SUBMIT ALL NECESSARY SAMPLES AND SHOP DRAWINGS TO THE DESIGNER FOR APPROVAL.
4. ALL CONCEPTS, DESIGNS, DETAILS, DRAWINGS AND SPECIFICATIONS ARE STUDENT WORK, AND THE PROPERTY OF THE DESIGNER. AS SUCH, THEY ARE NOT INTENDED FOR USE ON OTHER PROJECTS OR EXTENSIONS OF THE SPECIFIED PROJECT WHATSOEVER.

OWNERSHIP. ALL DRAWINGS, SPECIFICATIONS, DESIGNS & COPIES THEROF ARE THE PROPERTY OF THE DESIGNER AND THE OWNER, WHETHER OR NOT THE WORK FOR WHICH THEY ARE MADE IS PERFORMED, AND ARE NOT TO BE USED OR DUPLICATED ON OTHER WORK EXCEPT BY WRITTEN CONSENT FROM THE DESIGNER AND OWNER.

REV	DESCRIPTION	DATE

PROJECT: ROYAL VICTORIA REGIONAL HEALTH CENTRE

ADDRESS: 201 GEORGIAN DR. BARRIE, ON L4M 6M2

DRAWING: LVL 2 FURNITURE PLAN

SHEET: ID-3


DESIGNED BY: KP, CL, TG

ISSUE DATE: 04.09.2026

COURSE: INDE 3005

SCALE: As indicated

2026-11-08 2:27:03 PM

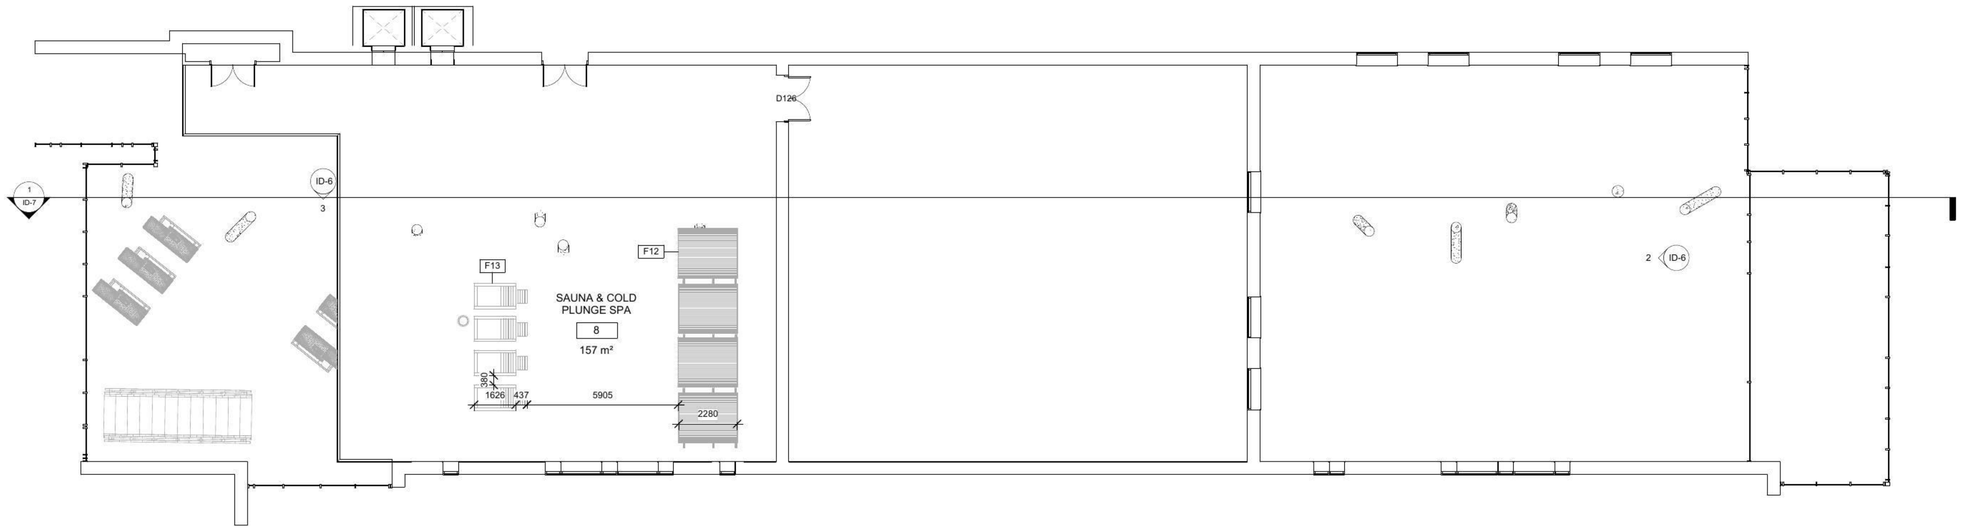

1 LVL 3 RCP
1 : 100

FF&E Schedule

Tag	Description	Materials	Manufacturer	Quantity
F1	Sofa w Built-In Table	Polyester, Maple Finish	Stance Healthcare	1
F2	Accessible Sofa	Cotton, Maple Wood	Custom	7
F3	Cafe Booths	Plastic(PTFE), Maple Wood	Custom	8
F4	Cafe Seating	Stainless Steel(Black), Wood	Steelcase Health	20
F5	Rounded Cafe Booths	Plastic(PTFE), Maple Wood	Custom	2
F6	Architectural Built-In	Maple Wood	Custom	1
F7	Built-In Bar	Maple Wood, Cladded	Medmill	1
F9	Bar Seating	Stainless Steel(Black), Wood	Steelcase Health	9
F10	Beanbag Seating	Polyester, Cotton	Stance Healthcare	4
F11	Armchair	Cotton, Maple Wood Finish	Stance Healthcare	2
F12	Reclining 'Beach' Chair	Cotton, Maple Wood	Stance Healthcare	6
F13	Sauna	Cedar, Hemlock	True North Saunas	4
F14	Cold Plunge	Stainless Steel, Cedar	IceWorksBath	4

Design ATELIER
(705) 826-4266
1 GEORGIAN DR. BARRIE, ON

GENERAL NOTES:

1. THE CONTRACTOR AND ALL SUB-CONTRACTORS SHALL VERIFY ALL DIMENSIONS, DETAILS AND SPECIFICATIONS ON SITE AND REPORT ALL DISCREPANCIES IN WRITING TO THE DESIGNER BEFORE PROCEEDING WITH THE WORK.
2. DRAWINGS ARE NOT TO BE SCALED.
3. THE CONTRACTOR AND SUB-CONTRACTORS, BEFORE PROCEEDING WITH THE WORK, MUST SUBMIT ALL NECESSARY SAMPLES AND SHOP DRAWINGS TO THE DESIGNER FOR APPROVAL.
4. ALL CONCEPTS, DESIGNS, DETAILS, DRAWINGS AND SPECIFICATIONS ARE STUDENT WORK, AND THE PROPERTY OF THE DESIGNER, AS SUCH, THEY ARE NOT INTENDED FOR USE ON OTHER PROJECTS OR EXTENSIONS OF THE SPECIFIED PROJECT WHATSOEVER.

OWNERSHIP. ALL DRAWINGS, SPECIFICATIONS, DESIGNS & COPIES THEROF ARE THE PROPERTY OF THE DESIGNER AND THE OWNER, WHETHER OR NOT THE WORK FOR WHICH THEY ARE MADE IS PERFORMED, AND ARE NOT TO BE USED OR DUPLICATED ON OTHER WORK EXCEPT BY WRITTEN CONSENT FROM THE DESIGNER AND OWNER.

REV	DESCRIPTION	DATE

PROJECT: ROYAL VICTORIA REGIONAL HEALTH CENTRE

ADDRESS: 201 GEORGIAN DR.
BARRIE, ON L4M 6M2

DRAWING: LVL 3 FURNITURE PLAN

SHEET: ID-3.1


DESIGNED BY: KP, CL, TG

ISSUE DATE: 04.09.2026

COURSE: INDE 3005

SCALE: As indicated

2026-11-08 2:27:25 PM

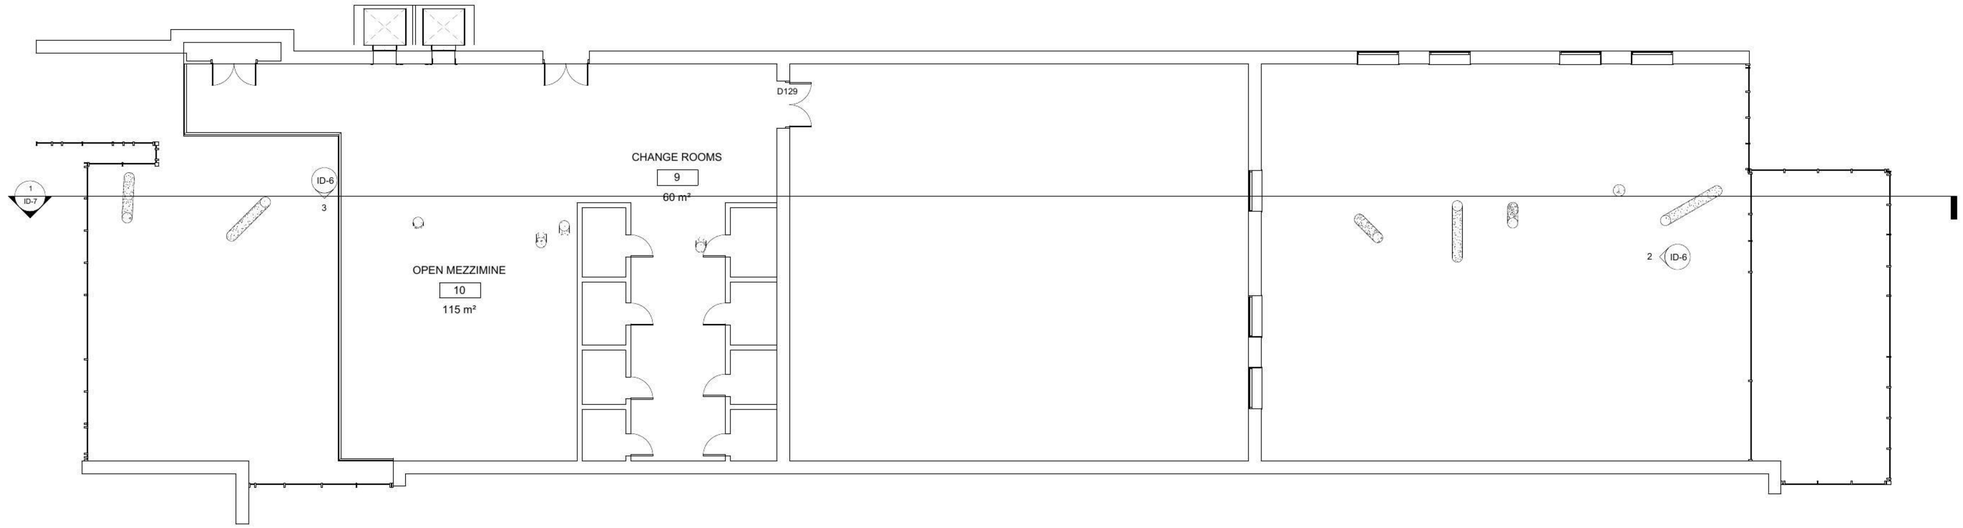

1 LVL 4 FURNITURE PLAN
1 : 100

FF&E Schedule

Tag	Description	Materials	Manufacturer	Quantity
F1	Sofa w Built-In Table	Polyester, Maple Finish	Stance Healthcare	1
F2	Accessible Sofa	Cotton, Maple Wood	Custom	7
F3	Cafe Booths	Plastic(PTFE), Maple Wood	Custom	8
F4	Cafe Seating	Stainless Steel(Black), Wood	Steelcase Health	20
F5	Rounded Cafe Booths	Plastic(PTFE), Maple Wood	Custom	2
F6	Architectural Built-In	Maple Wood	Custom	1
F7	Built-In Bar	Maple Wood, Cladded	Medmill	1
F9	Bar Seating	Stainless Steel(Black), Wood	Steelcase Health	9
F10	Beanbag Seating	Polyester, Cotton	Stance Healthcare	4
F11	Armchair	Cotton, Maple Wood Finish	Stance Healthcare	2
F12	Reclining 'Beach' Chair	Cotton, Maple Wood	Stance Healthcare	6
F13	Sauna	Cedar, Hemlock	True North Saunas	4
F14	Cold Plunge	Stainless Steel, Cedar	IceWorksBath	4

Design ATELIER
(705) 826-4206
1 GEORGIAN DR. BARRIE, ON

GENERAL NOTES:

1. THE CONTRACTOR AND ALL SUB-CONTRACTORS SHALL VERIFY ALL DIMENSIONS, DETAILS AND SPECIFICATIONS ON SITE AND REPORT ALL DISCREPANCIES IN WRITING TO THE DESIGNER BEFORE PROCEEDING WITH THE WORK.
2. DRAWINGS ARE NOT TO BE SCALED.
3. THE CONTRACTOR AND SUB-CONTRACTORS, BEFORE PROCEEDING WITH THE WORK, MUST SUBMIT ALL NECESSARY SAMPLES AND SHOP DRAWINGS TO THE DESIGNER FOR APPROVAL.
4. ALL CONCEPTS, DESIGNS, DETAILS, DRAWINGS AND SPECIFICATIONS ARE STUDENT WORK AND THE PROPERTY OF THE DESIGNER. AS SUCH, THEY ARE NOT INTENDED FOR USE ON OTHER PROJECTS OR EXTENSIONS OF THE SPECIFIED PROJECT WHATSOEVER.

OWNERSHIP. ALL DRAWINGS, SPECIFICATIONS, DESIGNS & COPIES THEROF ARE THE PROPERTY OF THE DESIGNER AND THE OWNER, WHETHER OR NOT THE WORK FOR WHICH THEY ARE MADE IS PERFORMED, AND ARE NOT TO BE USED OR DUPLICATED ON OTHER WORK EXCEPT BY WRITTEN CONSENT FROM THE DESIGNER AND OWNER.

REV.	DESCRIPTION	DATE

PROJECT: ROYAL VICTORIA REGIONAL HEALTH CENTRE

ADDRESS: 201 GEORGIAN DR. BARRIE, ON L4M 6M2

DRAWING: LVL 4 FURNITURE PLAN

SHEET: ID-3.2


DESIGNED BY: KP, CL, TG

ISSUE DATE: 04.09.2026

COURSE: INDE 3005

SCALE: As indicated

2026-11-08 2:27:27 PM

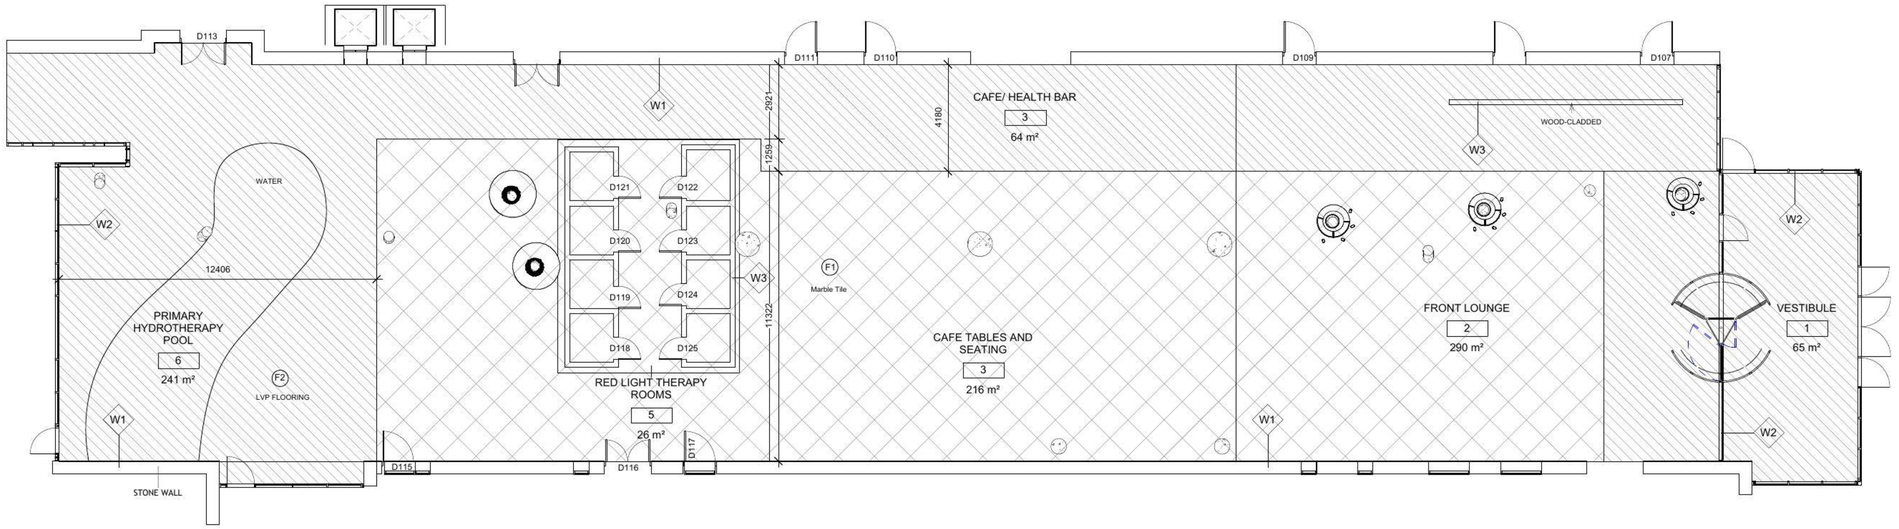

1 LVL 2 FINISHES PLAN

1 : 100

Finish Schedule			
Tag	Description	Materials	Manufacturer
W1	Exterior Wall	Paint	Sherwin Willliams
W1	Interior Wall	Stone	Dekko
W2	Curtain Walls	Glass	Custom
W3	Interior Partition	Wood Cladded Wall	Branch Architectural Systems
W4	Interior Partition	Stone	Dekko
F1	Flooring	Marble Tile	Geoceramica
F2	Flooring	LVP Flooring	Interface
C1	Ceilings	Drywall 3340 mm A.F.F	Phoenix Drywall

Finishes Legend

- (F1) Marble Tile
- (F2) LVP Flooring

Design ATELIER
(705) 826-4206
1 GEORGIAN DR. BARRIE, ON

GENERAL NOTES:

1. THE CONTRACTOR AND ALL SUB-CONTRACTORS SHALL VERIFY ALL DIMENSIONS, DETAILS AND SPECIFICATIONS ON SITE AND REPORT ALL DISCREPANCIES IN WRITING TO THE DESIGNER BEFORE PROCEEDING WITH THE WORK.
2. DRAWINGS ARE NOT TO BE SCALED.
3. THE CONTRACTOR AND SUB-CONTRACTORS, BEFORE PROCEEDING WITH THE WORK, MUST SUBMIT ALL NECESSARY SAMPLES AND SHOP DRAWINGS TO THE DESIGNER FOR APPROVAL.
4. ALL CONCEPTS, DESIGNS, DETAILS, DRAWINGS AND SPECIFICATIONS ARE STUDENT WORK AND THE PROPERTY OF THE DESIGNER. AS SUCH, THEY ARE NOT INTENDED FOR USE ON OTHER PROJECTS OR EXTENSIONS OF THE SPECIFIED PROJECT WHATSOEVER.

OWNERSHIP. ALL DRAWINGS, SPECIFICATIONS, DESIGNS & COPIES THEROF ARE THE PROPERTY OF THE DESIGNER AND THE OWNER, WHETHER OR NOT THE WORK FOR WHICH THEY ARE MADE IS PERFORMED, AND ARE NOT TO BE USED OR DUPLICATED ON OTHER WORK EXCEPT BY WRITTEN CONSENT FROM THE DESIGNER AND OWNER.

REV	DESCRIPTION	DATE

PROJECT: ROYAL VICTORIA REGIONAL HEALTH CENTRE

ADDRESS: 201 GEORGIAN DR. BARRIE, ON L4M 6M2

DRAWING: FINISHES PLAN

SHEET: ID-4


DESIGNED BY: KP, CL, TG

ISSUE DATE: 04.09.2026

COURSE: INDE 3005

SCALE: As indicated

2026-11-08 2:27:49 PM

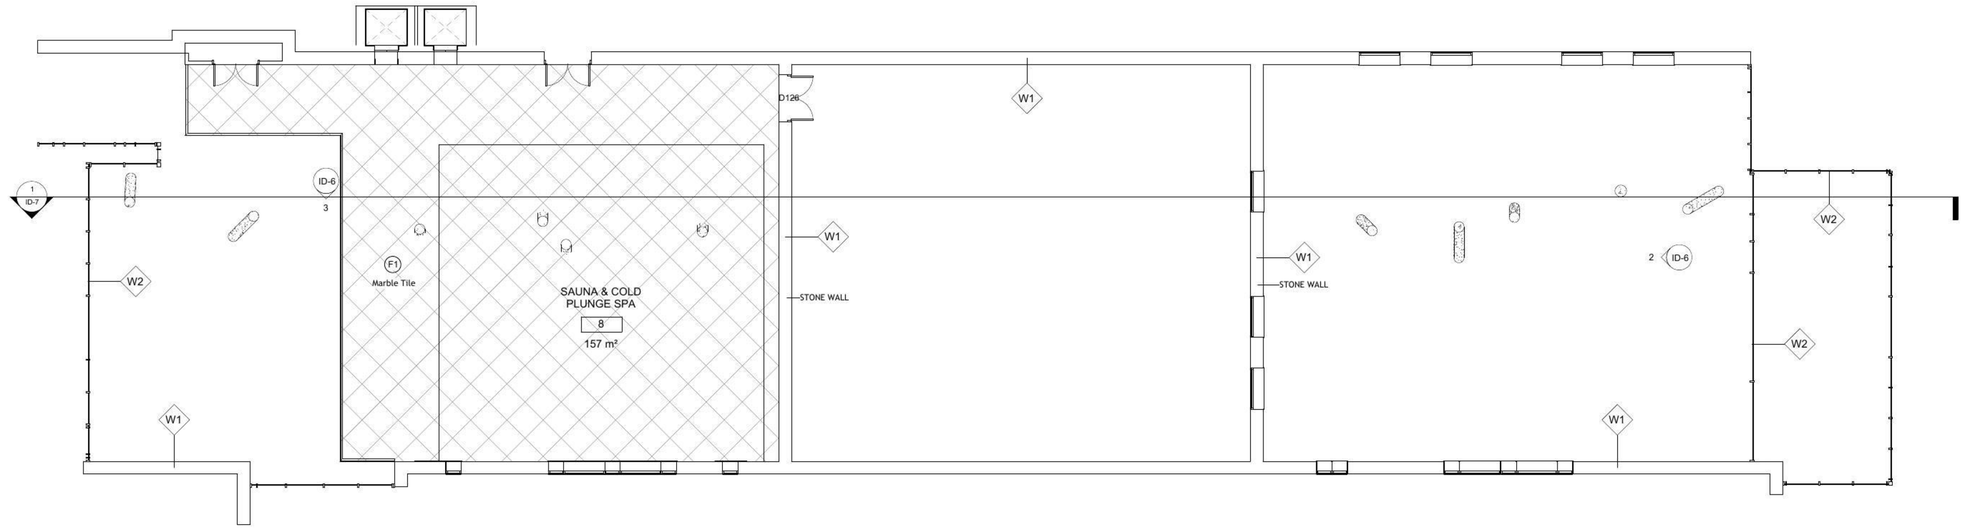

1 LVL 3 FINISHES PLAN
1 : 100

Finish Schedule			
Tag	Description	Materials	Manufacturer
W1	Exterior Wall	Paint	Sherwin Willliams
W1	Interior Wall	Stone	Dekko
W2	Curtain Walls	Glass	Custom
W3	Interior Partition	Wood Cladded Wall	Branch Architectural Systems
W4	Interior Partition	Stone	Dekko
F1	Flooring	Marble Tile	Geoceramica
F2	Flooring	LVP Flooring	Interface
C1	Ceilings	Drywall 3340 mm A.F.F	Phoenix Drywall

Finishes Legend

- (F1) Marble Tile
- (F2) LVP Flooring

Design ATELIER
(705) 826-4206
1 GEORGIAN DR. BARRIE, ON

GENERAL NOTES:

1. THE CONTRACTOR AND ALL SUB-CONTRACTORS SHALL VERIFY ALL DIMENSIONS, DETAILS AND SPECIFICATIONS ON SITE AND REPORT ALL DISCREPANCIES IN WRITING TO THE DESIGNER BEFORE PROCEEDING WITH THE WORK.
2. DRAWINGS ARE NOT TO BE SCALED.
3. THE CONTRACTOR AND SUB-CONTRACTORS, BEFORE PROCEEDING WITH THE WORK, MUST SUBMIT ALL NECESSARY SAMPLES AND SHOP DRAWINGS TO THE DESIGNER FOR APPROVAL.
4. ALL CONCEPTS, DESIGNS, DETAILS, DRAWINGS AND SPECIFICATIONS ARE STUDENT WORK AND THE PROPERTY OF THE DESIGNER. AS SUCH, THEY ARE NOT INTENDED FOR USE ON OTHER PROJECTS OR EXTENSIONS OF THE SPECIFIED PROJECT WHATSOEVER.

OWNERSHIP. ALL DRAWINGS, SPECIFICATIONS, DESIGNS & COPIES THEROF ARE THE PROPERTY OF THE DESIGNER AND THE OWNER, WHETHER OR NOT THE WORK FOR WHICH THEY ARE MADE IS PERFORMED, AND ARE NOT TO BE USED OR DUPLICATED ON OTHER WORK EXCEPT BY WRITTEN CONSENT FROM THE DESIGNER AND OWNER.

REV	DESCRIPTION	DATE

PROJECT: ROYAL VICTORIA REGIONAL HEALTH CENTRE

ADDRESS: 201 GEORGIAN DR.
BARRIE, ON L4M 6M2

DRAWING: FINISHES PLAN

SHEET: ID-4.1


DESIGNED BY: KP, CL, TG

ISSUE DATE: 04.09.2026

COURSE: INDE 3005

SCALE: As indicated

2026-11-06 2:27:50 PM

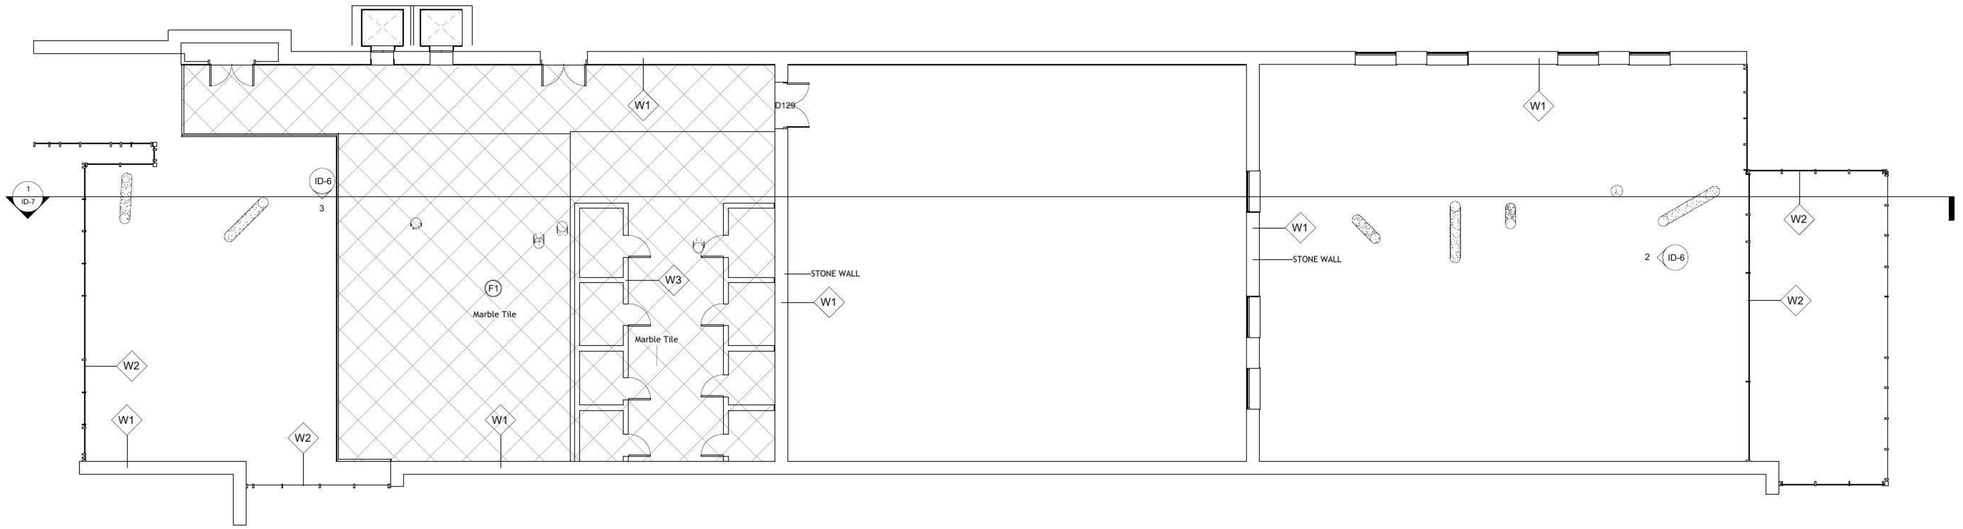

1 LVL 4 FINISHES PLAN

1 : 100

Finish Schedule			
Tag	Description	Materials	Manufacturer
W1	Exterior Wall	Paint	Sherwin Willliams
W1	Interior Wall	Stone	Dekko
W2	Curtain Walls	Glass	Custom
W3	Interior Partition	Wood Cladded Wall	Branch Architectural Systems
W4	Interior Partition	Stone	Dekko
F1	Flooring	Marble Tile	Geoceramica
F2	Flooring	LVP Flooring	Interface
C1	Ceilings	Drywall 3340 mm A.F.F	Phoenix Drywall

Finishes Legend

(F1) Marble Tile

(F2) LVP Flooring

Design ATELIER

(705) 826-4206
1 GEORGIAN DR. BARRIE, ON

GENERAL NOTES:

1. THE CONTRACTOR AND ALL SUB-CONTRACTORS SHALL VERIFY ALL DIMENSIONS, DETAILS AND SPECIFICATIONS ON SITE AND REPORT ALL DISCREPANCIES IN WRITING TO THE DESIGNER BEFORE PROCEEDING WITH THE WORK.
2. DRAWINGS ARE NOT TO BE SCALED.
3. THE CONTRACTOR AND SUB-CONTRACTORS, BEFORE PROCEEDING WITH THE WORK, MUST SUBMIT ALL NECESSARY SAMPLES AND SHOP DRAWINGS TO THE DESIGNER FOR APPROVAL.
4. ALL CONCEPTS, DESIGNS, DETAILS, DRAWINGS AND SPECIFICATIONS ARE STUDENT WORK AND THE PROPERTY OF THE DESIGNER. AS SUCH, THEY ARE NOT INTENDED FOR USE ON OTHER PROJECTS OR EXTENSIONS OF THE SPECIFIED PROJECT WHATSOEVER.

OWNERSHIP: ALL DRAWINGS, SPECIFICATIONS, DESIGNS & COPIES THEROF ARE THE PROPERTY OF THE DESIGNER AND THE OWNER, WHETHER OR NOT THE WORK FOR WHICH THEY ARE MADE IS PERFORMED, AND ARE NOT TO BE USED OR DUPLICATED ON OTHER WORK EXCEPT BY WRITTEN CONSENT FROM THE DESIGNER AND OWNER.

REV	DESCRIPTION	DATE

PROJECT: ROYAL VICTORIA REGIONAL HEALTH CENTRE

ADDRESS: 201 GEORGIAN DR. BARRIE, ON L4M 6M2

DRAWING: FINISHES PLAN

SHEET: ID-4.2


DESIGNED BY: KP, CL, TG

ISSUE DATE: 04.09.2026


COURSE: INDE 3005

SCALE: As indicated

2026-11-08 2:27:51 PM

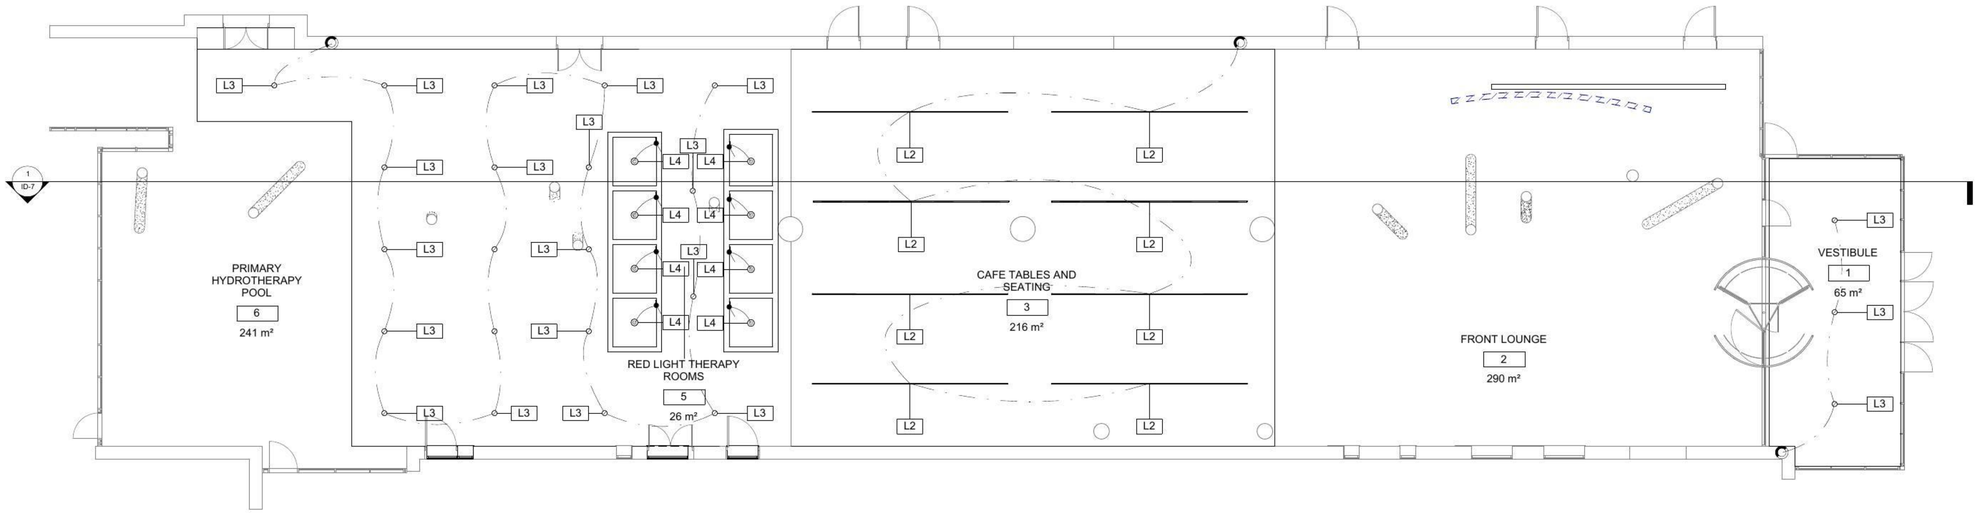

1 MAIN LVL RCP
1 : 100

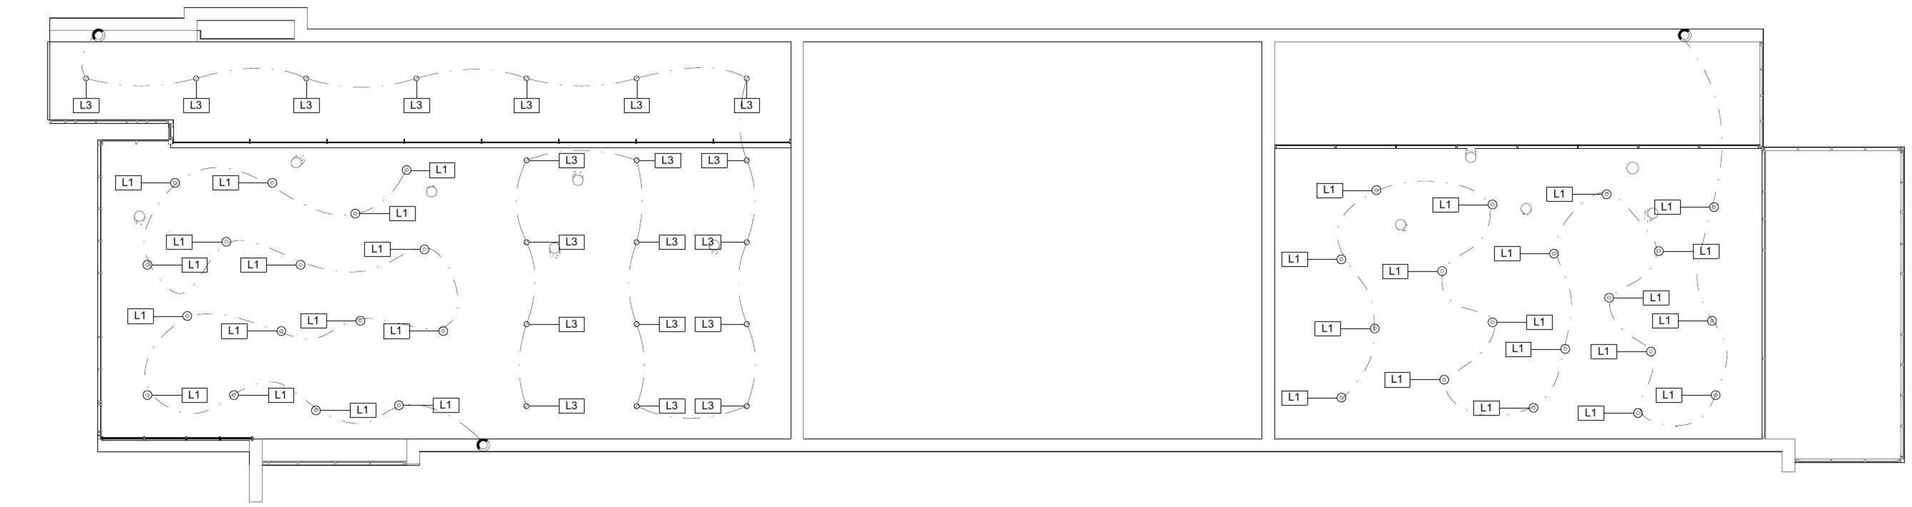

2 LVL 5 RCP
1 : 100

Design ATELIER

(705) 826-4206
1 GEORGIAN DR. BARRIE, ON

GENERAL NOTES:

1. THE CONTRACTOR AND ALL SUB-CONTRACTORS SHALL VERIFY ALL DIMENSIONS, DETAILS AND SPECIFICATIONS ON SITE AND REPORT ALL DISCREPANCIES IN WRITING TO THE DESIGNER BEFORE PROCEEDING WITH THE WORK.
2. DRAWINGS ARE NOT TO BE SCALED.
3. THE CONTRACTOR AND SUB-CONTRACTORS, BEFORE PROCEEDING WITH THE WORK, MUST SUBMIT ALL NECESSARY SAMPLES AND SHOP DRAWINGS TO THE DESIGNER FOR APPROVAL.
4. ALL CONCEPTS, DESIGNS, DETAILS, DRAWINGS AND SPECIFICATIONS ARE STUDENT WORK AND THE PROPERTY OF THE DESIGNER. AS SUCH, THEY ARE NOT INTENDED FOR USE ON OTHER PROJECTS OR EXTENSIONS OF THE SPECIFIED PROJECT WHATSOEVER.

OWNERSHIP: ALL DRAWINGS, SPECIFICATIONS, DESIGNS & COPIES THEROF ARE THE PROPERTY OF THE DESIGNER AND THE OWNER, WHETHER OR NOT THE WORK FOR WHICH THEY ARE MADE IS PERFORMED, AND ARE NOT TO BE USED OR DUPLICATED ON OTHER WORK EXCEPT BY WRITTEN CONSENT FROM THE DESIGNER AND OWNER.

REV.	DESCRIPTION	DATE

PROJECT:
ROYAL VICTORIA REGIONAL HEALTH CENTRE

ADDRESS:
201 GEORGIAN DR.
BARRIE, ON L4M 6M2

DRAWING:
REFLECTED CEILING PLAN

SHEET:
ID-5


DESIGNED BY:
KP, CL, TG

ISSUE DATE:
04.09.2026

COURSE:
INDE 3005

SCALE:
1 : 100

2026-11-08 2:27:53 PM

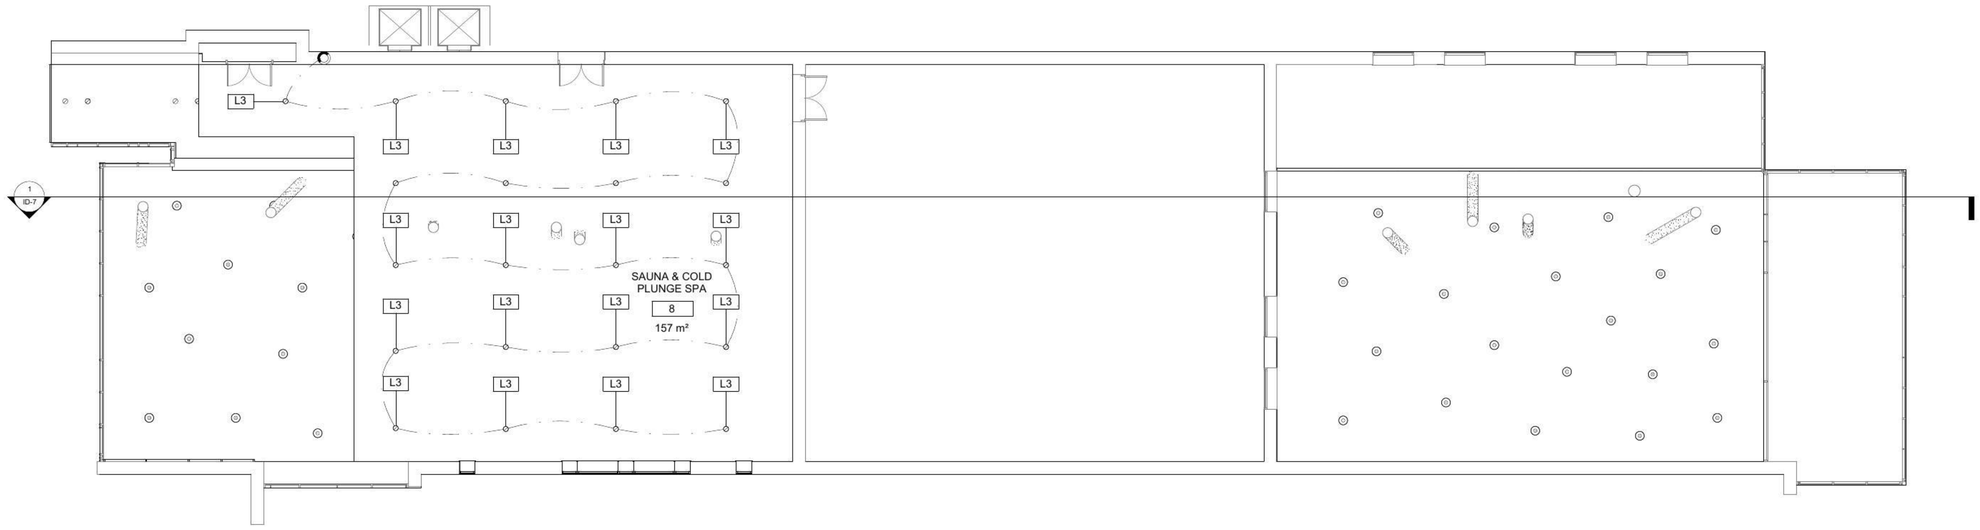

1 LVL 3 RCP
1 : 100

Note all sprinkler systems and fire systems will remain the same as it was prior to any renovations completed.

Lighting Fixture Schedule

Type Mark	Family	Type	Count	Level	Description
L4	Lighting_Fixtures_Pendant_3	135mm_Radius-60_Watt_Incandescent	8	LEVEL 4	
L1	Lighting_Fixtures_Pendant_3	175mm_Radius-100_Watt_Incandescent	35	LEVEL 5	
L3	Downlight - Recessed Can	203mm Incandescent - 230V	23	MAIN LEVEL	
L3	Downlight - Recessed Can	203mm Incandescent - 230V	23	LVL 3 RCP	
L3	Downlight - Recessed Can	203mm Incandescent - 230V	19	LEVEL 5	
L2	Lighting_Fixtures_Recessed_Lamp_Linear_LED	300mm	8	MAIN LEVEL	

Ceiling Schedule

Ceiling Type	Material	Finish	Height
C1	Drywall 3340 mm A.F.F	Flat Paint	As per plan and section dimensions

SYMBOL LEGEND

SYMBOL	USAGE
	CEILING RECESSED LIGHT
	CEILING PENDENT LIGHT
	ONE WAY LIGHT SWITCH
	TIMER LIGHT SWITCH
	WIRING

SYMBOL LEGEND
1 : 50

Design ATELIER
(705) 826-4206
1 GEORGIAN DR. BARRIE, ON

GENERAL NOTES:

1. THE CONTRACTOR AND ALL SUB-CONTRACTORS SHALL VERIFY ALL DIMENSIONS, DETAILS AND SPECIFICATIONS ON SITE AND REPORT ALL DISCREPANCIES IN WRITING TO THE DESIGNER BEFORE PROCEEDING WITH THE WORK.
2. DRAWINGS ARE NOT TO BE SCALED.
3. THE CONTRACTOR AND SUB-CONTRACTORS, BEFORE PROCEEDING WITH THE WORK, MUST SUBMIT ALL NECESSARY SAMPLES AND SHOP DRAWINGS TO THE DESIGNER FOR APPROVAL.
4. ALL CONCEPTS, DESIGNS, DETAILS, DRAWINGS AND SPECIFICATIONS ARE STUDENT WORK AND THE PROPERTY OF THE DESIGNER. AS SUCH, THEY ARE NOT INTENDED FOR USE ON OTHER PROJECTS OR EXTENSIONS OF THE SPECIFIED PROJECT WHATSOEVER.

OWNERSHIP. ALL DRAWINGS, SPECIFICATIONS, DESIGNS & COPIES THEROF ARE THE PROPERTY OF THE DESIGNER AND THE OWNER, WHETHER OR NOT THE WORK FOR WHICH THEY ARE MADE IS PERFORMED, AND ARE NOT TO BE USED OR DUPLICATED ON OTHER WORK EXCEPT BY WRITTEN CONSENT FROM THE DESIGNER AND OWNER.

REV	DESCRIPTION	DATE

PROJECT:
ROYAL VICTORIA REGIONAL HEALTH CENTRE

ADDRESS:
201 GEORGIAN DR.
BARRIE, ON L4M 6M2

DRAWING:
REFLECTED CEILING PLAN

SHEET:
ID-5.1


DESIGNED BY:
KP, CL, TG

ISSUE DATE:
04.09.2026


COURSE:
INDE 3005

SCALE:
As indicated


2026-11-08 2:27:55 PM

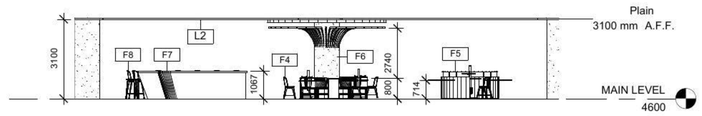

1 CAFE ELEVATION
1 : 100

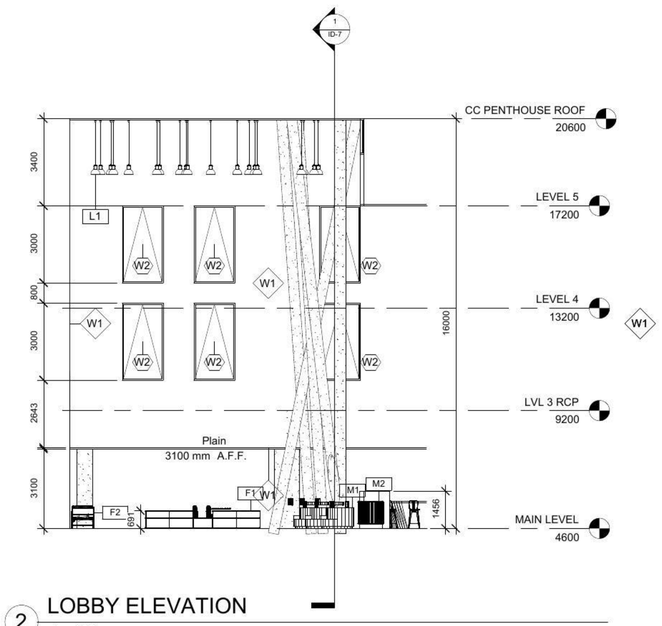

2 LOBBY ELEVATION
1 : 100

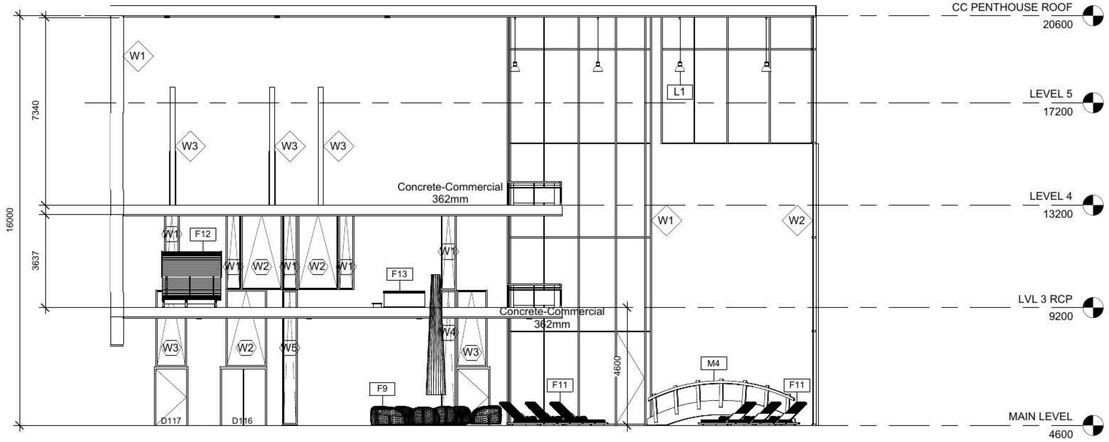

3 HYDRO SPA ELEVATION
1 : 100

Design ATELIER

(705) 826-4266
1 GEORGIAN DR. BARRIE, ON

GENERAL NOTES:

1. THE CONTRACTOR AND ALL SUB-CONTRACTORS SHALL VERIFY ALL DIMENSIONS, DETAILS AND SPECIFICATIONS ON SITE AND REPORT ALL DISCREPANCIES IN WRITING TO THE DESIGNER BEFORE PROCEEDING WITH THE WORK.
2. DRAWINGS ARE NOT TO BE SCALED.
3. THE CONTRACTOR AND SUB-CONTRACTORS, BEFORE PROCEEDING WITH THE WORK, MUST SUBMIT ALL NECESSARY SAMPLES AND SHOP DRAWINGS TO THE DESIGNER FOR APPROVAL.
4. ALL CONCEPTS, DESIGNS, DETAILS, DRAWINGS AND SPECIFICATIONS ARE STUDENT WORK, AND THE PROPERTY OF THE DESIGNER. AS SUCH, THEY ARE NOT INTENDED FOR USE ON OTHER PROJECTS OR EXTENSIONS OF THE SPECIFIED PROJECT WHATSOEVER.

OWNERSHIP: ALL DRAWINGS, SPECIFICATIONS, DESIGNS & COPIES THEROF ARE THE PROPERTY OF THE DESIGNER AND THE OWNER, WHETHER OR NOT THE WORK FOR WHICH THEY ARE MADE IS PERFORMED, AND ARE NOT TO BE USED OR DUPLICATED ON OTHER WORK EXCEPT BY WRITTEN CONSENT FROM THE DESIGNER AND OWNER.

REV	DESCRIPTION	DATE

PROJECT:
ROYAL VICTORIA REGIONAL HEALTH CENTRE

ADDRESS:
201 GEORGIAN DR.
BARRIE, ON L4M 6M2

DRAWING:
INTERIOR ELEVATIONS

SHEET:
ID-6


DESIGNED BY:
KP, CL, TG

ISSUE DATE:
04.09.2026

COURSE:
INDE 3005

SCALE:
1 : 100

2026-11-08 2:28:46 PM

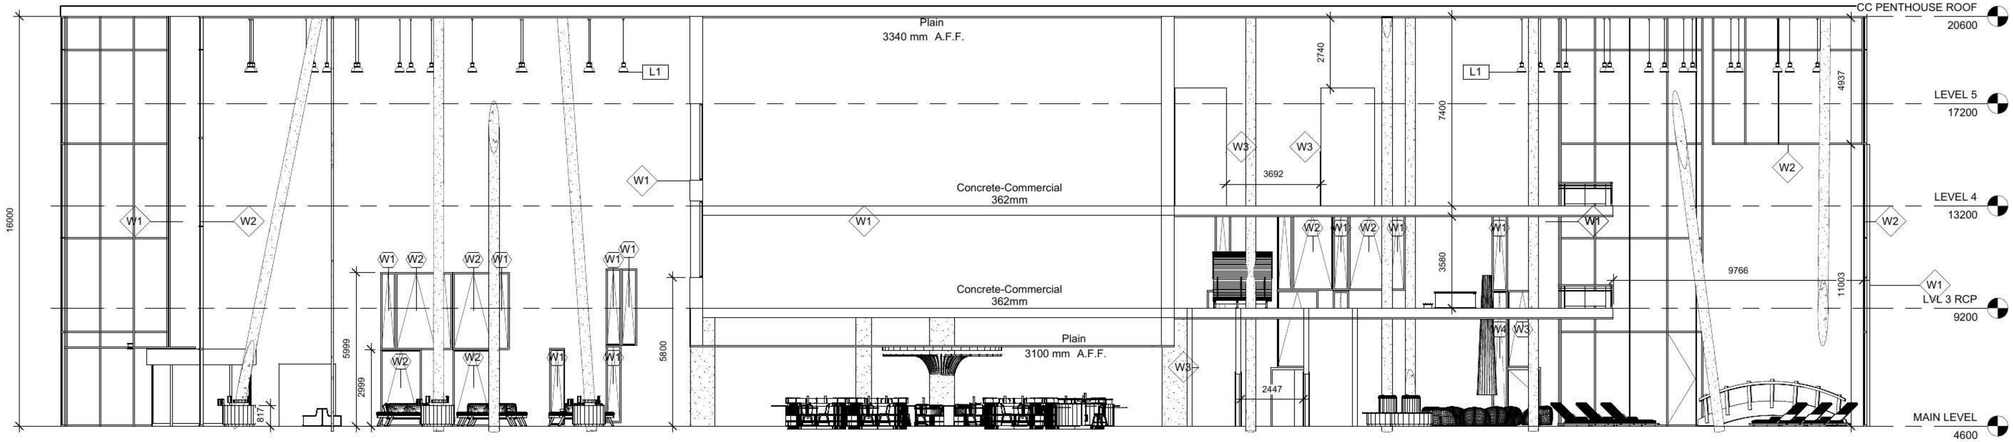

1 SECTION
1 : 100

Design ATELIER

(705) 826-4206
1 GEORGIAN DR. BARRIE, ON

GENERAL NOTES:

1. THE CONTRACTOR AND ALL SUB-CONTRACTORS SHALL VERIFY ALL DIMENSIONS, DETAILS AND SPECIFICATIONS ON SITE AND REPORT ALL DISCREPANCIES IN WRITING TO THE DESIGNER BEFORE PROCEEDING WITH THE WORK.
2. DRAWINGS ARE NOT TO BE SCALED.
3. THE CONTRACTOR AND SUB-CONTRACTORS, BEFORE PROCEEDING WITH THE WORK, MUST SUBMIT ALL NECESSARY SAMPLES AND SHOP DRAWINGS TO THE DESIGNER FOR APPROVAL.
4. ALL CONCEPTS, DESIGNS, DETAILS, DRAWINGS AND SPECIFICATIONS ARE STUDENT WORK AND THE PROPERTY OF THE DESIGNER. AS SUCH, THEY ARE NOT INTENDED FOR USE ON OTHER PROJECTS OR EXTENSIONS OF THE SPECIFIED PROJECT WHATSOEVER.

OWNERSHIP: ALL DRAWINGS, SPECIFICATIONS, DESIGNS & COPIES THEROF ARE THE PROPERTY OF THE DESIGNER AND THE OWNER, WHETHER OR NOT THE WORK FOR WHICH THEY ARE MADE IS PERFORMED, AND ARE NOT TO BE USED OR DUPLICATED ON OTHER WORK EXCEPT BY WRITTEN CONSENT FROM THE DESIGNER AND OWNER.

REV	DESCRIPTION	DATE

PROJECT:
ROYAL VICTORIA REGIONAL HEALTH CENTRE

ADDRESS:
201 GEORGIAN DR.
BARRIE, ON L4M 6M2

DRAWING:
SECTIONS

SHEET:
ID-7

DESIGNED BY:
KP, CL, TG

ISSUE DATE:
04.09.2026

COURSE:
INDE 3005

SCALE:
1 : 100

2026-11-08 2:29:29 PM